

IP "Nur Stroy Consulting"
Design Company



IP "Nur Stroy Consulting" Jobalau
Company

SKETCH DESIGN

9-story residential building located at: Atyrau,
Nursaya microdistrict, street No. 11, No. 6/1




Director of IP "Nur Stroy Consulting"

Nurmukhanbetova A.A.

Customer:

Karimov A.N.

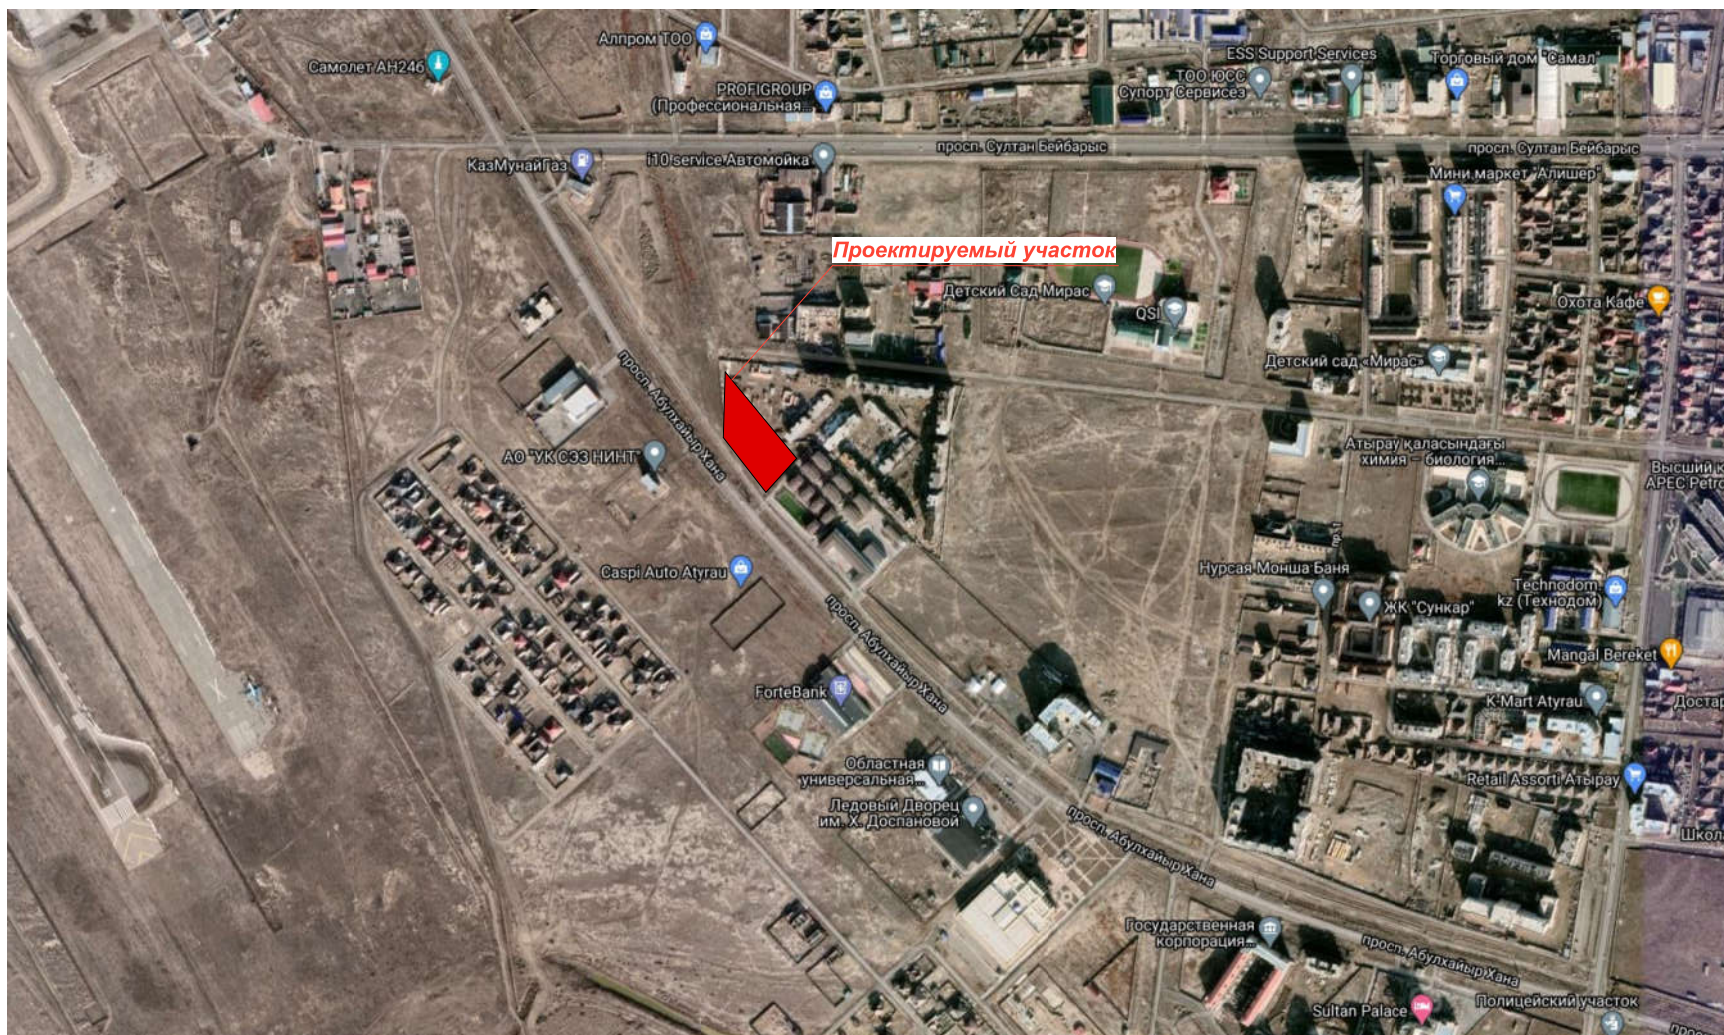

Должность	Ф.И.О	Подп.	Дата	Эскизный проект девятиэтажного жилого дома по адресу: мкр. Нурсая, ул.№11, №6/1	Стадия	Лист	Листов
исполн.					ЭП		
заказчик	Каримов А.Н.			Общие данные	ИП "Nur Stroy Consulting"		

Technical and economic indicators:

A residential complex consisting of two twin blocks

The designed residential complex provides



Commercial space (ground floor) and residential space (floors 2 through 9). The residential complex will include a mini-children's center for one group and a medical center, with an area of approximately 33.5 square meters.

TEP of the project:

1. Number of storeys 9;
2. Construction volume 65,101.9 m³ including:
 - 2.1. aboveground part 56,364.6 m³;
 - 2.2. underground part 8737.3 m³;
3. Building area 2831.6 m²;
4. The total area of the building is 15,605.6 m², including:
 - 4.1. The total area of the residential building is 11,984.8 m²;
 - 4.2. Total area of public spaces is 1,308.8 m²;
6. Usable area for public use 1,235.8 m²;
7. Estimated area for public use is 1,179.6 m²;
8. Total area of apartments is 9648.0 m²;
9. The living area of the apartments is 5004.8 m²;
10. There are 112 apartments in the entire building, including:
 - 10.1. one-room apartments 32;
 - 10.2. two-room apartments - 32;
 - 10.3. three-room apartments - 48;

Должность	Ф.И.О	Подп.	Дата	Эскизный проект девятиэтажного жилого дома по адресу: мкр. Нурсая, ул.№11, №6/1	Стадия	Лист	Листов
					ЭП		
исполн.					ИИ "Nur Stroy Consulting"		
заказчик	Каримов А.Н.						

Разбивочный план М 1 : 1000

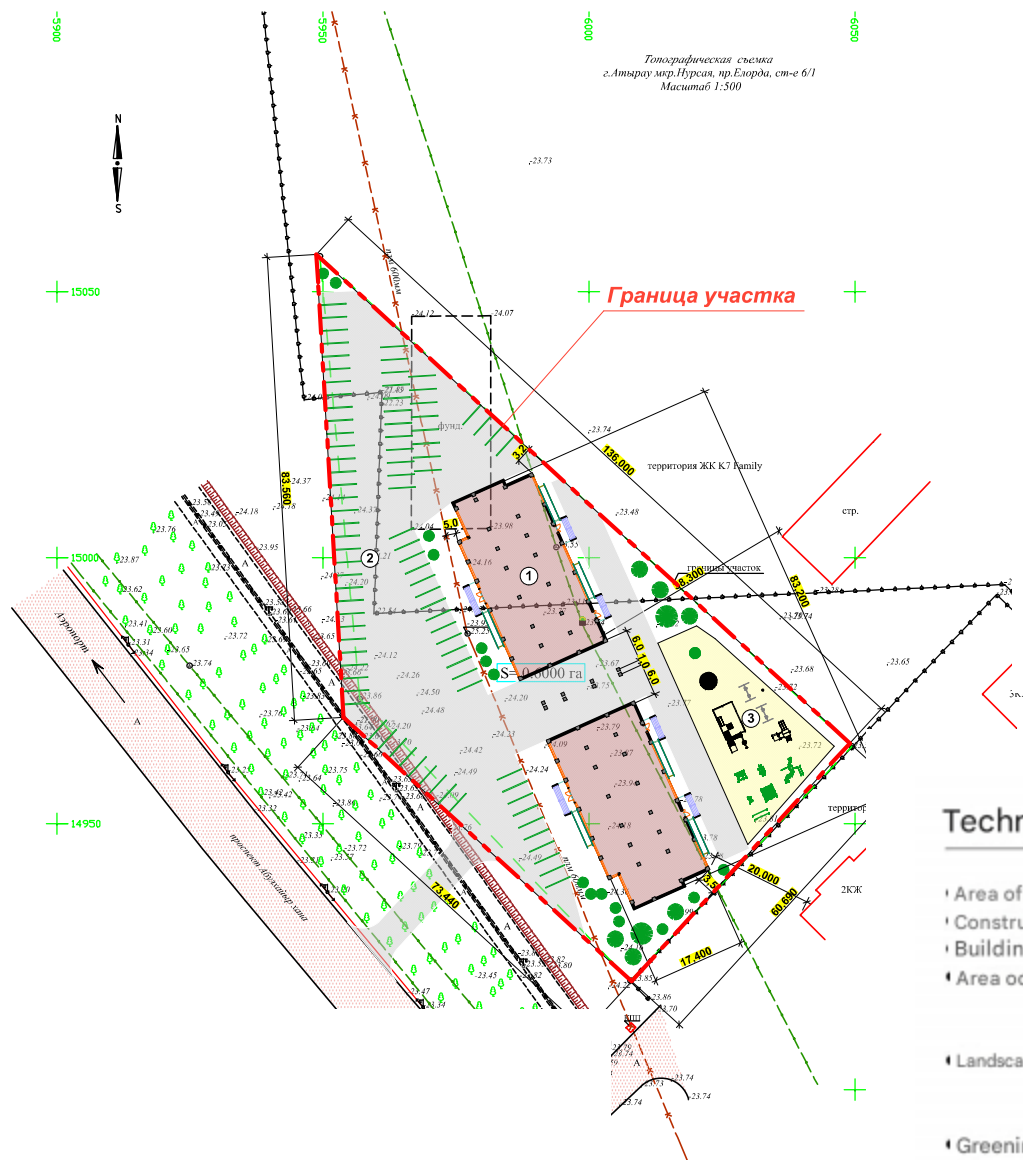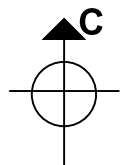

Explication:

- 1 - Designed object
- 2 - Parking for 120 spaces
- 3 - Children's and sports playground

Technical indicators:

Area of the enterprise territory -	0.6000 ha
Construction area -	2831.6 m ² ;
Building density -	63 %;
Area occupied by hard surface areas	1,693 m ² , including:
	on the ground - 801 m ² ;
	along the stylobate - 892 m ² ;
Landscaping area -	313 m ² , including:
	on the ground - 290 m ² ;
	along the stylobate - 23 m ² ;
Greening coefficient -	7 %.
The area occupied by existing roads is	537.4 m ²
Area of land used	4,460 m ²
Used territory coefficient	100 %

Note

- For general instructions, see sheet GP-1.
- The level of the finished floor of the 1st floor is taken as the 0.00 mark, which corresponds to the absolute mark of 309.14.
- All dimensions are in meters.
- The dimensions of the parking space are adopted in accordance with SP RK 3.03-105-2014 "Car Parking" clause 4.3.1.3 (taking into account the minimum permissible safety gaps) - 5.5 m x 2.5 m; for use by persons with disabilities - 6.0 m x 3.6 m.

Должность	Ф.И.О				жилого дома по адресу: мкр. Нурсая, ул.№11, №6/1	ЭП	3	
Исполн.								
Заказчик	Каримов А.Н.				Разбивочный план М 1 : 1000			ИИ "Nur Stroy Consulting"


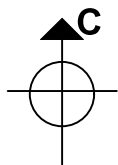


Схема генплана М 1 : 1000

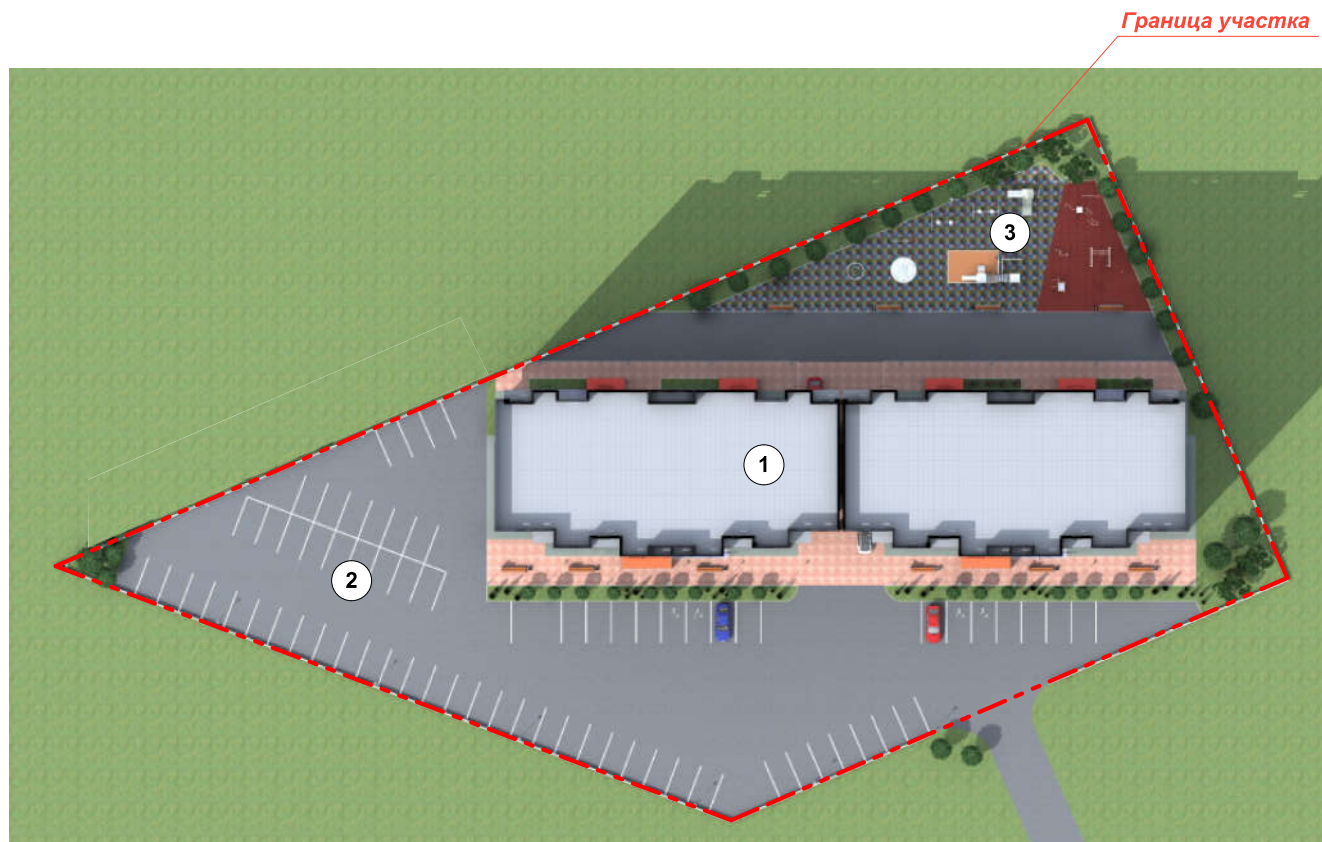

Граница участка

Explication:

- 1 - Designed object
- 2 - Parking for 120 spaces
- 3 - Children's and sports playground

Должность	Ф.И.О	Подп.	Дата	Эскизный проект девятиэтажного жилого дома по адресу: мкр. Нурсая, ул.№11, №6/1	Стадия	Лист	Листов
					ЭП		
исполн.				Схема генплана М 1 : 1000	ИИ "Nur Stroy Consulting"		
заказчик	Каримов А.Н.						

Перспектива



Атырау қалалық сәулет және қалақұрылысы бөлімінің басшысы

КЕЛІСІЛГЕН № 1397, 10.06.2021

<http://bp.eatyrau.kz/sedapi/userapp/1010345/stamp/62329/download>

Должность	Ф.И.О	Подп.	Дата	Эскизный проект девятиэтажного жилого дома по адресу: мкр. Нурсая, ул.№11, №6/1	Стадия	Лист	Листов
					ЭП		
исполн.				Перспектива	ИИ "Nur Stroy Consulting"		
заказчик	Каримов А.Н.						

Перспектива 2



Атырау қалалық сәулет және қалақұрылысы бөлімінің басшысы

КЕЛІСІЛГЕН № 1397, 10.06.2021

<http://bp.eatyrau.kz/sedapi/userapp/1010345/stamp/62329/download>

Должность	Ф.И.О	Подп.	Дата	Эскизный проект девятиэтажного жилого дома по адресу: мкр. Нурсая, ул.№11, №6/1	Стадия	Лист	Листов
исполн.					ЭП		
заказчик	Каримов А.Н.			Перспектива 2	ИП "Nur Stroy Consulting"		

Перспектива 3



Атырау қалалық сәулет және қалақұрылысы бөлімінің басшысы

КЕЛІСІЛГЕН № 1397, 10.06.2021

<http://bp.eatyrau.kz/sedapi/userapp/1010345/stamp/62329/download>

Должность	Ф.И.О	Подп.	Дата	Эскизный проект девятиэтажного жилого дома по адресу: мкр. Нурсая, ул.№11, №6/1	Стадия	Лист	Листов
исполн.					ЭП		
заказчик	Каримов А.Н.			Перспектива 3	ИИП "Nur Stroy Consulting"		

Перспектива 3



Атырау қалалық сәулет және қалақұрылысы бөлімінің басшысы

КЕЛІСІЛГЕН № 1397, 10.06.2021

<http://bp.eatyrau.kz/sedapi/userapp/1010345/stamp/62329/download>

Должность	Ф.И.О	Подп.	Дата	Эскизный проект девятиэтажного жилого дома по адресу: мкр. Нурсая, ул.№11, №6/1	Стадия	Лист	Листов
					ЭП		
исполн.				Перспектива 3	ИИ "Nur Stroy Consulting"		
заказчик	Каримов А.Н.						

Ночной вид



Атырау қалалық сәулет және қалақұрылысы бөлімінің басшысы

КЕЛІСІЛГЕН № 1397, 10.06.2021

<http://bp.eatyrau.kz/sedapi/userapp/1010345/stamp/62329/download>

Должность	Ф.И.О	Подп.	Дата	Эскизный проект девятиэтажного жилого дома по адресу: мкр. Нурсая, ул.№11, №6/1	Стадия	Лист	Листов
					ЭП		
исполн.				Ночной вид	ИИ "Nur Stroy Consulting"		
заказчик	Каримов А.Н.						

Главный фасад. М 1:100



Атырау қалалық сәулет және қалақұрылысы бөлімінің басшысы

КЕЛІСІЛГЕН № 1397, 10.06.2021

<http://bp.eatyrau.kz/sedapi/userapp/1010345/stamp/62329/download>

Должность	Ф.И.О	Подп.	Дата	Эскизный проект девятиэтажного жилого дома по адресу: мкр. Нурсая, ул.№11, №6/1	Стадия	Лист	Листов
					ЭП		
исполн.				Фасад в осях 1-2	ИИП "Nur Stroy Consulting"		
заказчик	Каримов А.Н.						

Боковой фасад. М 1:100




Атырау қалалық сәулет және қалақұрылысы бөлімінің басшысы

КЕЛІСІЛГЕН № 1397, 10.06.2021

<http://bp.eatyr.kz/sedapi/userapp/1010345/stamp/62329/download>

Должность	Ф.И.О	Подп.	Дата	Эскизный проект девятиэтажного жилого дома по адресу: мкр. Нурсая, ул.№11, №6/1	Стадия	Лист	Листов
					ЭП		
исполн.				Фасад в осях А-В	ИИ "Nur Stroy Consulting"		
заказчик	Каримов А.Н.						

Фасад здания. М 1:400

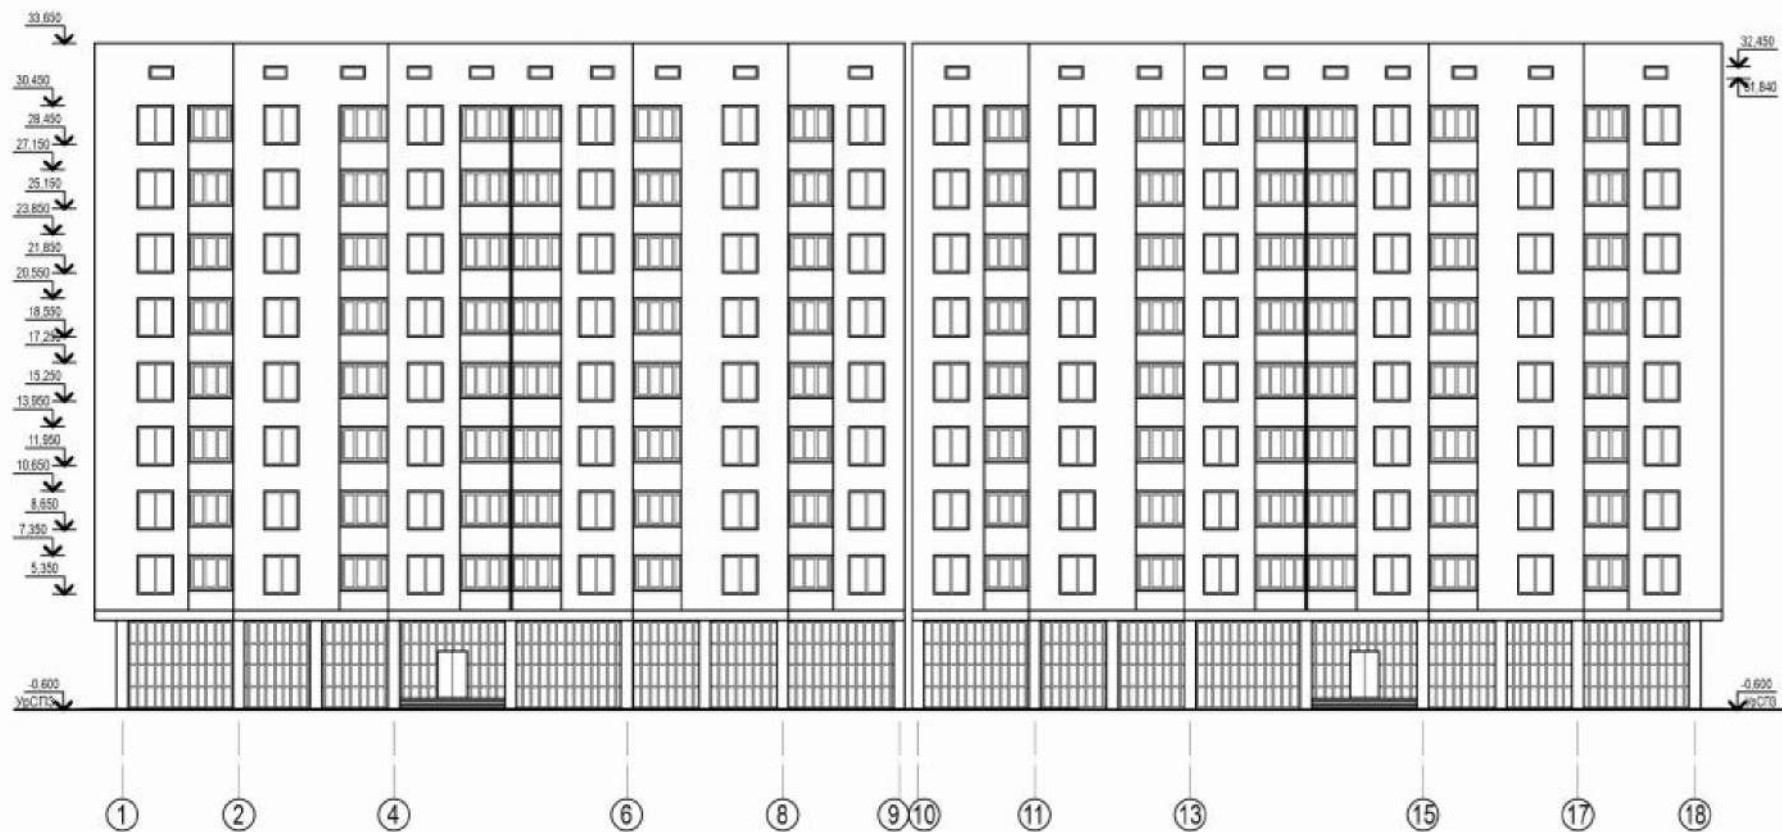

Должность	Ф.И.О	Подп.	Дата	Эскизный проект девятиэтажного жилого дома по адресу: мкр. Нурсая, ул.№11, №6/1	Стадия	Лист	Листов
					ЭП		
исполн.					ИИ "Nur Stroy Consulting"		
заказчик	Каримов А.Н.						


Атырау қалалық сәулет және қалақұрылысы бөлімінің басшысы

КЕЛІСІЛГЕН № 1397, 10.06.2021

<http://bp.eatyrau.kz/sedapi/userapp/1010345/stamp/62329/download>


План здания. М 1:400

План первого этажа

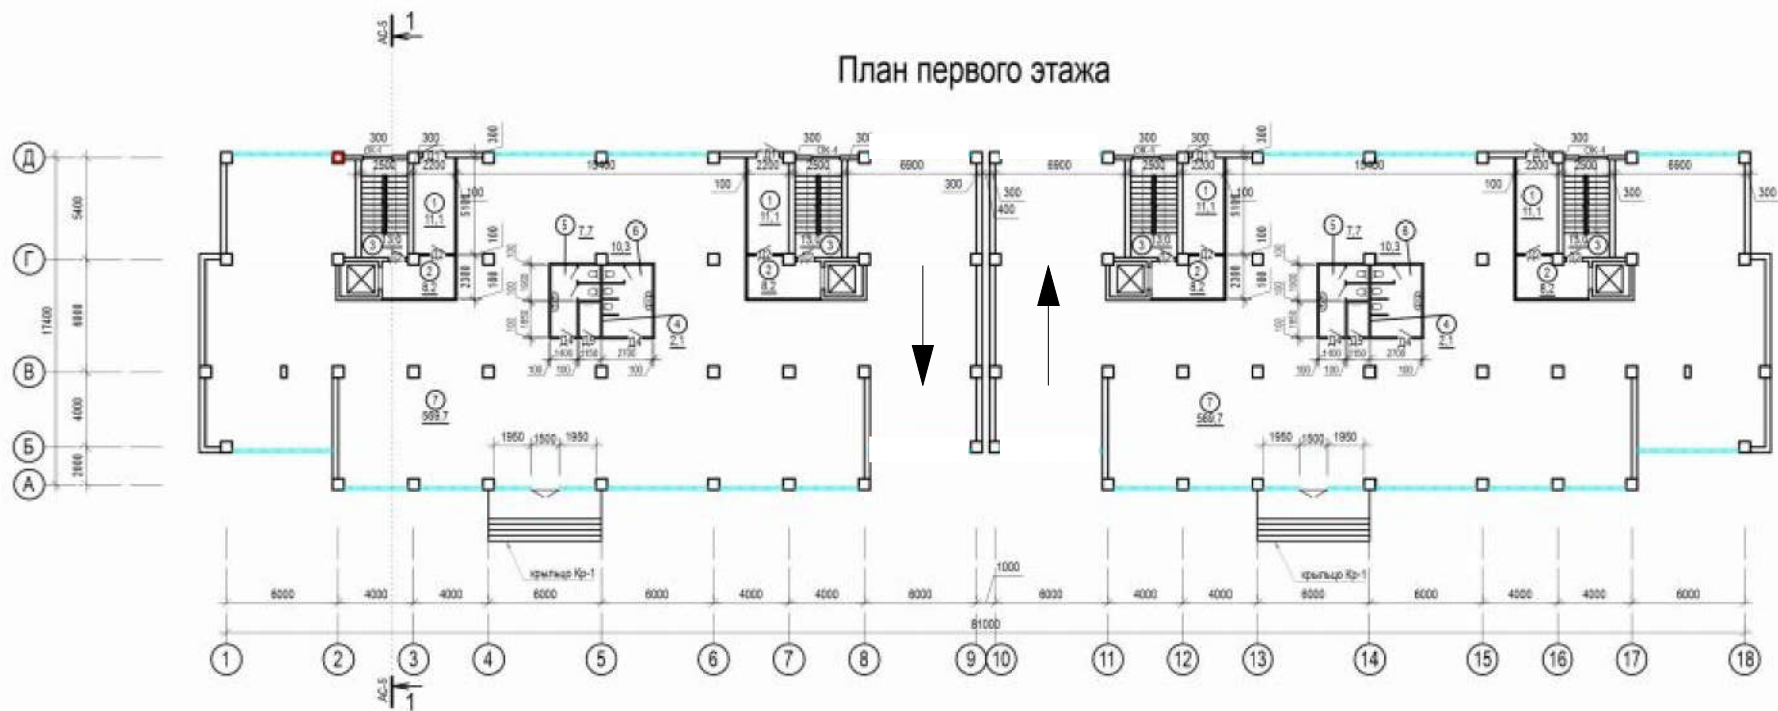

Должность	Ф.И.О	Подп.	Дата	Эскизный проект девятиэтажного жилого дома по адресу: мкр. Нурсая, ул.№11, №6/1	Стадия	Лист	Листов
исполн.					ЭП		
заказчик	Каримов А.Н.				ИИП "Nur Stroy Consulting"		

План здания. М 1:400

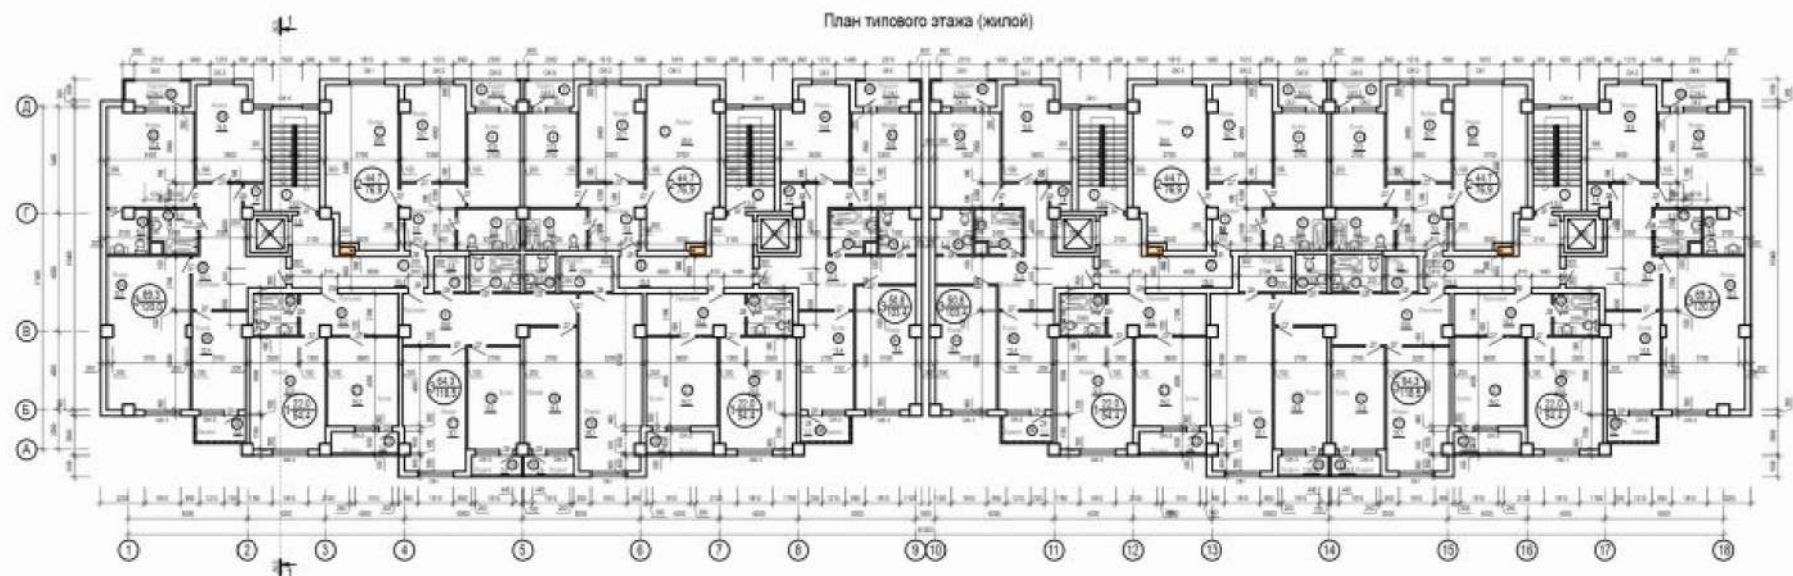

Должность	Ф.И.О	Подп.	Дата	Эскизный проект девятиэтажного жилого дома по адресу: мкр. Нурсая, ул.№11, №6/1	Стадия	Лист	Листов
					ЭП		
исполн.					ИП "Nur Stroy Consulting"		
заказчик	Каримов А.Н.						


Атырау қалалық сәулет және қалақұрылысы бөлімінің басшысы

КЕЛІСІЛГЕН № 1397, 10.06.2021

<http://bp.eatyrau.kz/sedapi/userapp/1010345/stamp/62329/download>

Разрез здания. М 1:400

Разрез 1-1

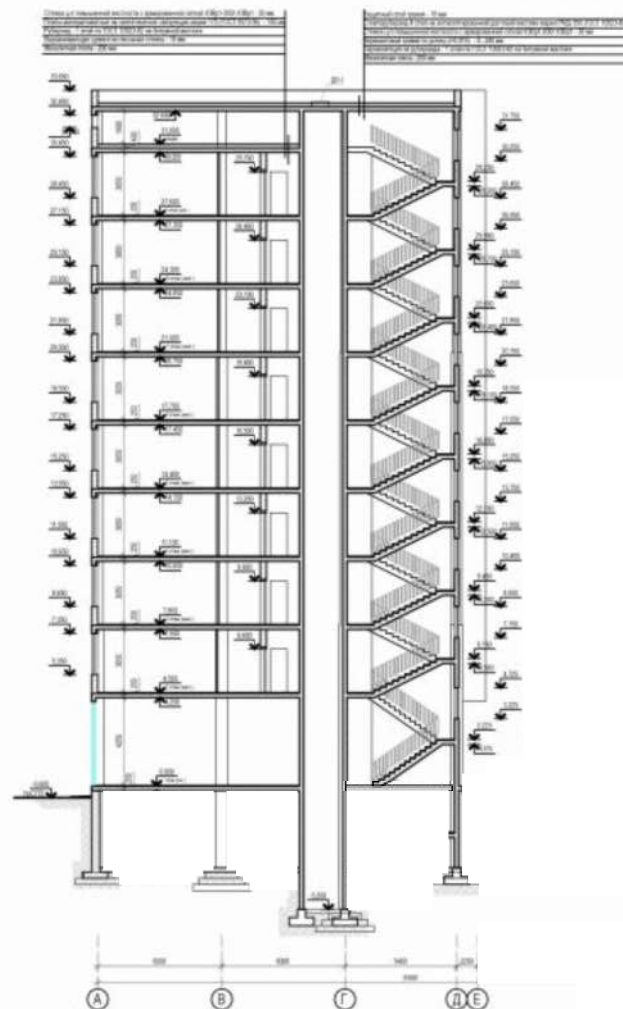

Атырау қалалық сәулет және қалақұрылысы бөлімінің басшысы

КЕЛІСІЛГЕН № 1397, 10.06.2021

<http://bp.eatyrau.kz/sedapi/userapp/1010345/stamp/62329/download>

Должность	Ф.И.О	Подп.	Дата	Эскизный проект девятиэтажного жилого дома по адресу: мкр. Нурсая, ул.№11, №6/1	Стадия	Лист	Листов
исполн.					ЭП		
заказчик	Каримов А.Н.				ИИ "Nur Stroy Consulting"		

План кровли. М 1:400



Должность	Ф.И.О	Подп.	Дата	Эскизный проект девятиэтажного жилого дома по адресу: мкр. Нурсая, ул.№11, №6/1	Стадия	Лист	Листов
					ЭП		
исполн.					ИИ "Nur Stroy Consulting"		
заказчик	Каримов А.Н.						

Атырау қалалық сәулет және қалақұрылысы бөлімінің басшысы

КЕЛІСІЛГЕН № 1397, 10.06.2021

<http://bp.eatyrau.kz/sedapi/userapp/1010345/stamp/62329/download>